




REPEATER SIGNAGE
TO BE PLACED
AT INTERSECTIONS

TMP MUST BE AUTHORISED
FOR IMPLEMENTATION BY
THE RELEVANT ROAD AUTHORITY



INTERSECTION SIGHT DISTANCE	SPEED RESTRICTION REQUIRED
300 - 181 m	80 kph
< 181 m	60 kph

'BURNING OFF' AND
'END OF BURN'
PANELS TO BE
CHANGED WHEN
NO BURNING
IS OCCURRING

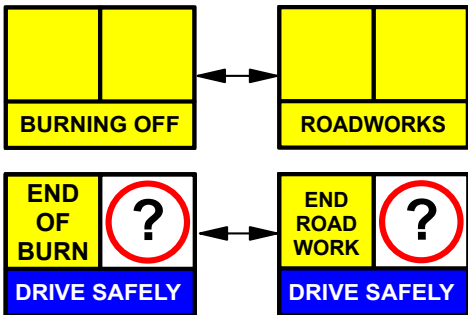

GENERAL NOTES:




- THIS TGS IS ONLY TO BE USED AS PART OF THIS GENERIC TRAFFIC MANAGEMENT PLAN
- ALL SIGN LOCATIONS ARE TO BE CHECKED PRIOR TO SETOUT AND POSITIONS ADJUSTED TO ALLOW FOR SPECIFIC SITE CONSTRAINTS SUCH AS VEGETATION, OTHER SIGNS, ROADSIDE FURNITURE AND SUFFICIENT SPACE ON SHOULDERS/EMERGENCY LANES.
- THE POSITIONS OF SIGNS, LENGTH OF TAPERS OR MARKING SHALL BE:
 - MINIMUM 10% LESS THAN THE DISTANCES OR LENGTHS GIVEN,
 - MAXIMUM 25% MORE THAN THE DISTANCES OR LENGTHS GIVEN.
- WHEN USING MMS ENSURE TWO 5mm THICK CORE FLUTE SIGNS ARE USED BACK TO BACK IN THE FRAME TO HELP PREVENT THE SIGN FROM BLOWING OUT
- USE OF FOLD UP SIGNS AND SWING SIGNS AND SIGNS ON ONE SIDE OF THE ROAD MAY BE ACCEPTABLE IN NARROW, VERY LOW VOLUME TRACKS <50 VPD

DISCLAIMER:

IT IS THE RESPONSIBILITY OF THE USER OF THIS TRAFFIC GUIDANCE SCHEME TO CONFIRM THE APPROPRIATENESS OR OTHERWISE FOR THE INTENDED WORK SITE BASED ON RIGOROUS RISK ASSESSMENT AND REVIEW OF THE REQUIREMENTS OF THE AS1742.3 AND MAIN ROADS WA TRAFFIC MANAGEMENT FOR WORKS ON ROADS CoP AND THE AGTTM. ALL RESPONSIBILITY WILL REMAIN WITH THE USER TO ENSURE COMPLIANCE WITH RELEVANT STANDARDS AND THE PROVISION OF THE NECESSARY LEVEL OF PROTECTION FOR WORK PERSONNEL AND WORK SITE.

DRAWN: MATTHEW BYRNE
AWTM CERT. No: AUS-AWTM-24-1367-05
SIGNED: *[Signature]*
REVIEWED: DALLAS MILLWARD
AWTM CERT. No: AUS-AWTM-23-2352-04
SIGNED: *[Signature]*

TABLE A	
POSTED SPEED km/h	SIGN SPACING m
50 OR LESS	30
60	45
70	140
80	160
90	180
100	200
110	220

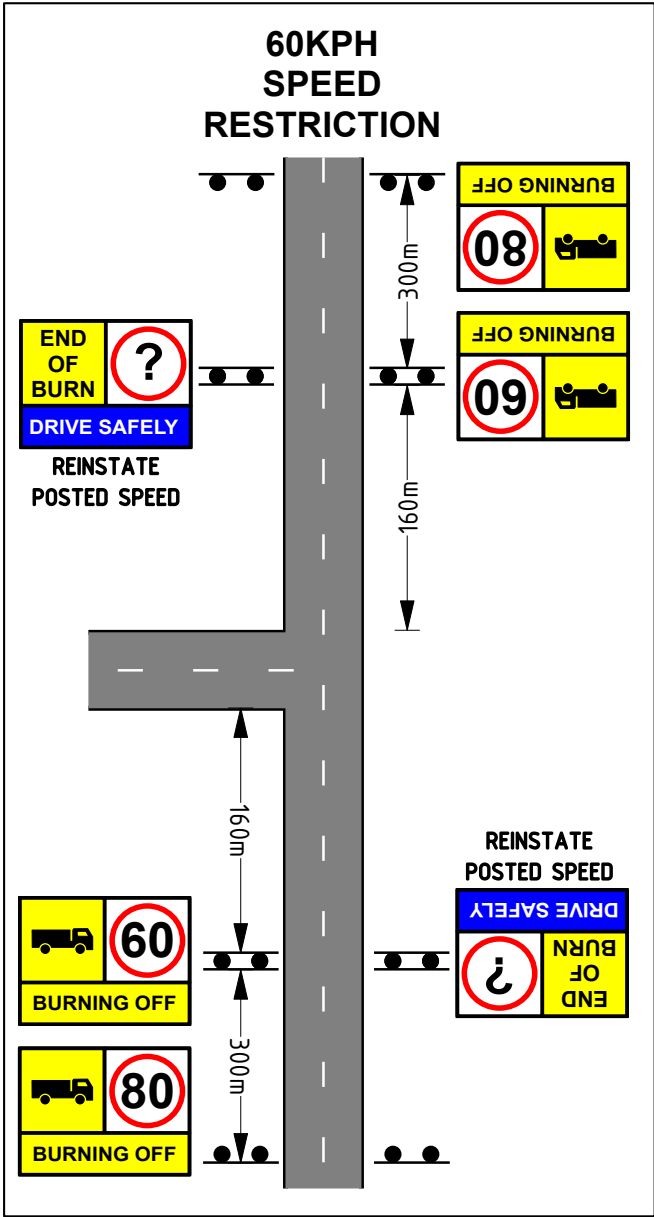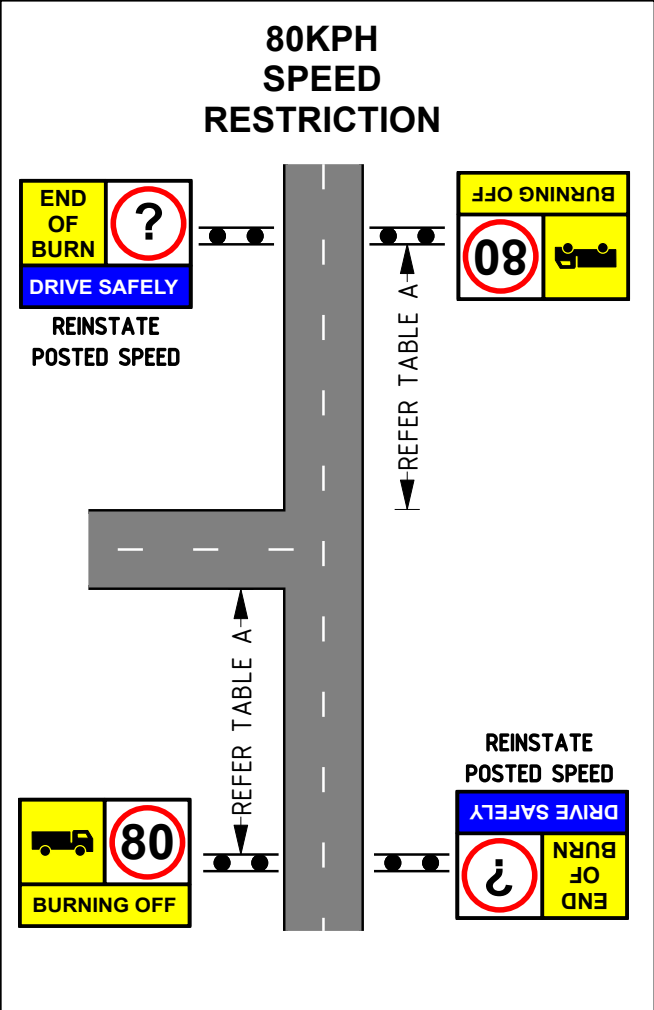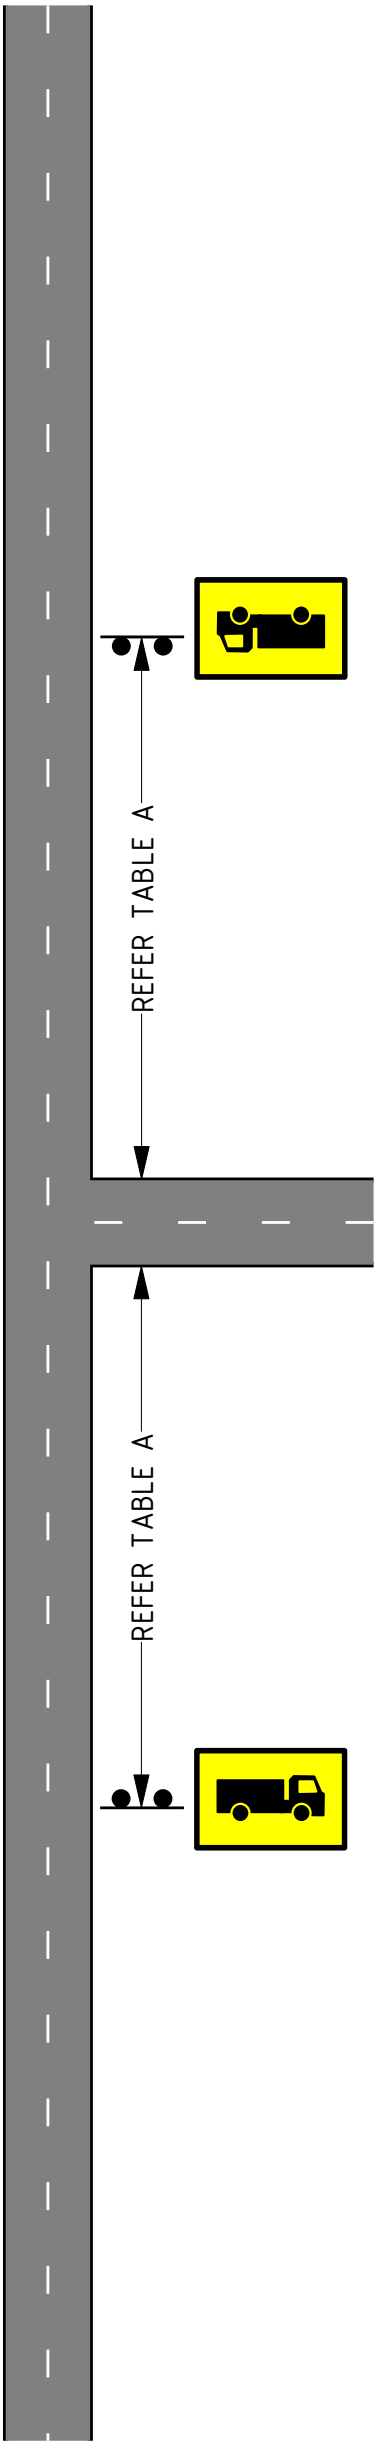

TRUCK MOVEMENTS

DATE: 25/03/2026 REV No: 1 BURN-26-22