

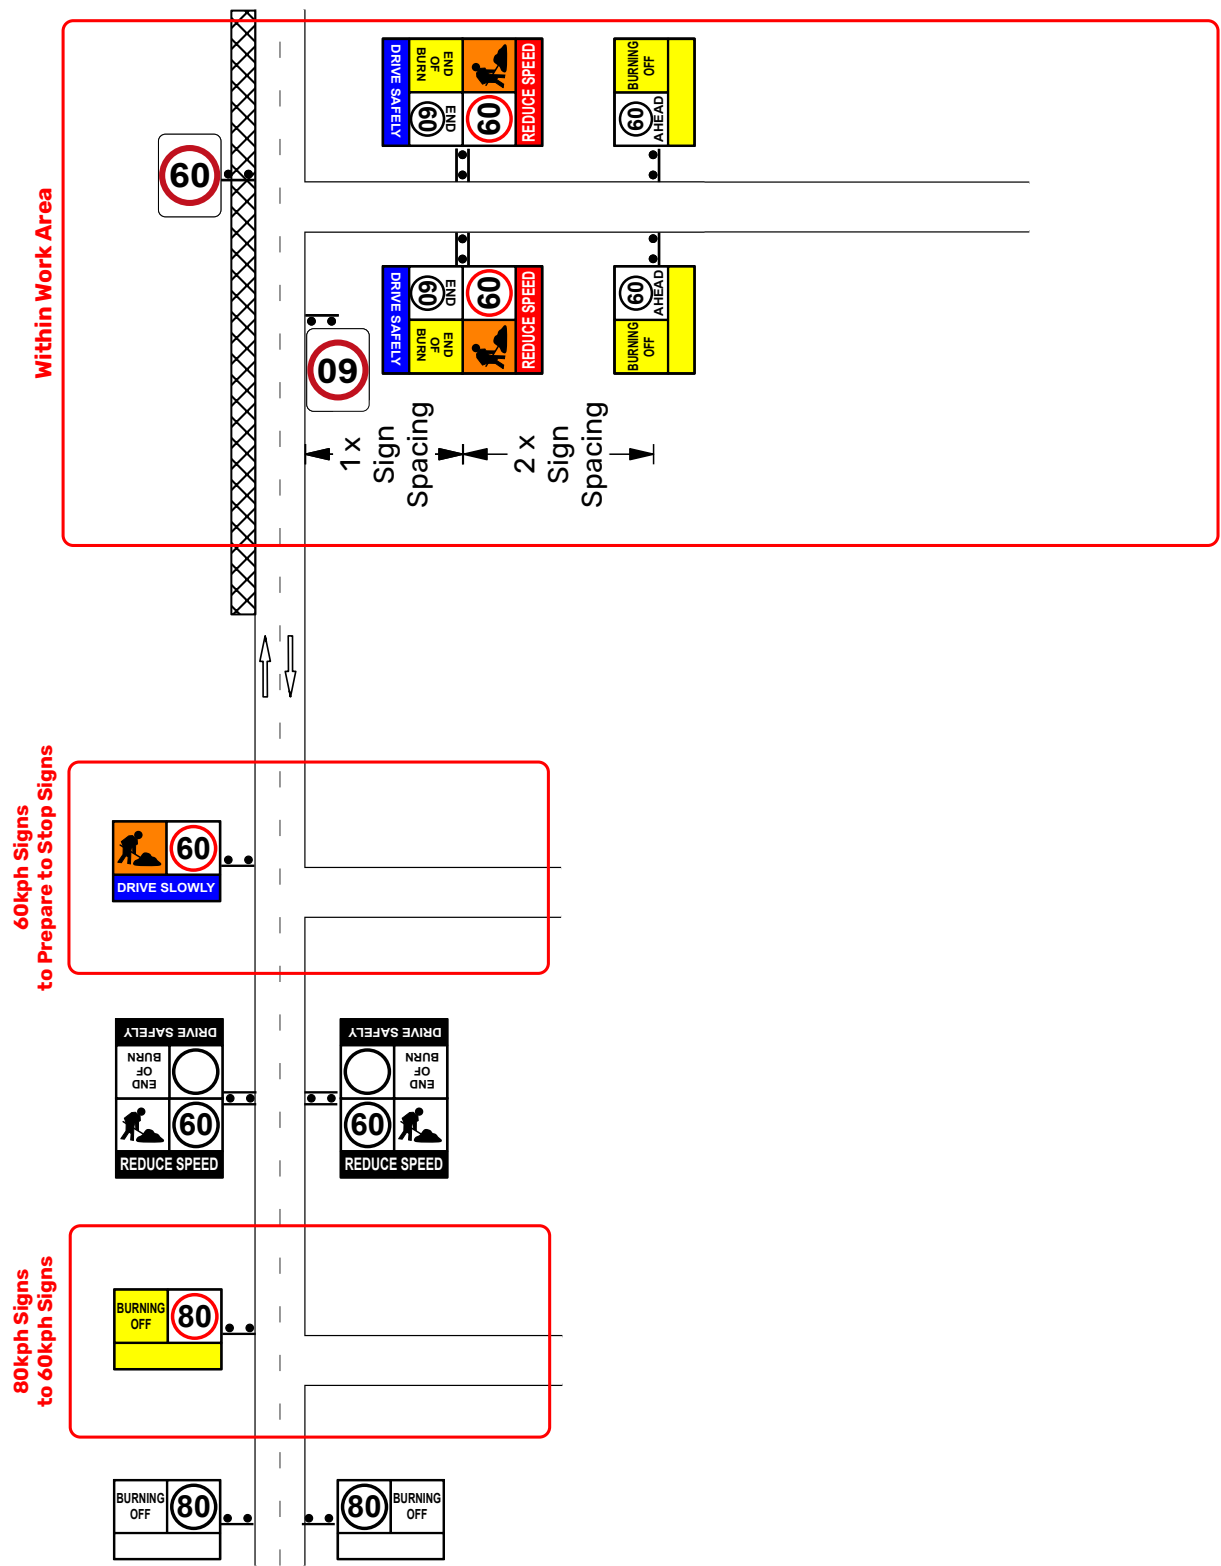


TABLE A	
POSTED SPEED km/h	SIGN SPACING m
50 OR LESS	30
60	45
70	140
80	160
90	180
100	200
110	220

DISCLAIMER:
IT IS THE RESPONSIBILITY OF THE USER OF THIS TRAFFIC GUIDANCE SCHEME TO CONFIRM THE APPROPRIATENESS OR OTHERWISE FOR THE INTENDED WORK SITE BASED ON RIGOROUS RISK ASSESSMENT AND REVIEW OF THE REQUIREMENTS OF THE AS1742.3 AND MAIN ROADS WA TRAFFIC MANAGEMENT FOR WORKS ON ROADS CoP AND THE AGTMM. ALL RESPONSIBILITY WILL REMAIN WITH THE USER TO ENSURE COMPLIANCE WITH RELEVANT STANDARDS AND THE PROVISION OF THE NECESSARY LEVEL OF PROTECTION FOR WORK PERSONNEL AND WORK SITE.

DRAWN: MATTHEW BYRNE
AWTM CERT. No: AUS-AWTM-24-1367-05
SIGNED: 

REVIEWED: DALLAS MILLWARD
AWTM CERT. No: AUS-AWTM-23-2352-04
SIGNED: 

SIDE ROAD SCHEME